PELAN CADANGAN PENGAMBILAN TANAH SEKSYEN 8 DI BAWAH 3(1)(b)
AKTA PENGAMBILAN TANAH 1960 (AKTA 486)
BAGI KERJA MEMBINA DAN MENYIAPKAN KOLAM AIR BUKIT KULAI
BERKAPASITI 18.2 JUTA LITER
MUKIM SENAI
DAERAH KULAI
NEGERI JOHOR DARUL TA'ZIM


AGENSI PENGAMBIL : RANHILL SAJ


Pelan No : JA(J)01_2025 RANHILL BUKIT KULAI/LA/PELAN INDEKS REV.1
JA(J)01_2025 RANHILL BUKIT KULAI/LA/SEKSYEN 8 REV.1

JURUKUR TANAH

JURUKUR ABADI

Topographical, Cadastral, Engineering Survey Services
Land Development Consultant
No.6-1, Jalan Padi Emas 4/5
Pusat Bandar Tampoi
81200 Johor Bahru
Tel 07-2387244 Fax 07-2380235
E-mail: jurukur_abadi@yahoo.com

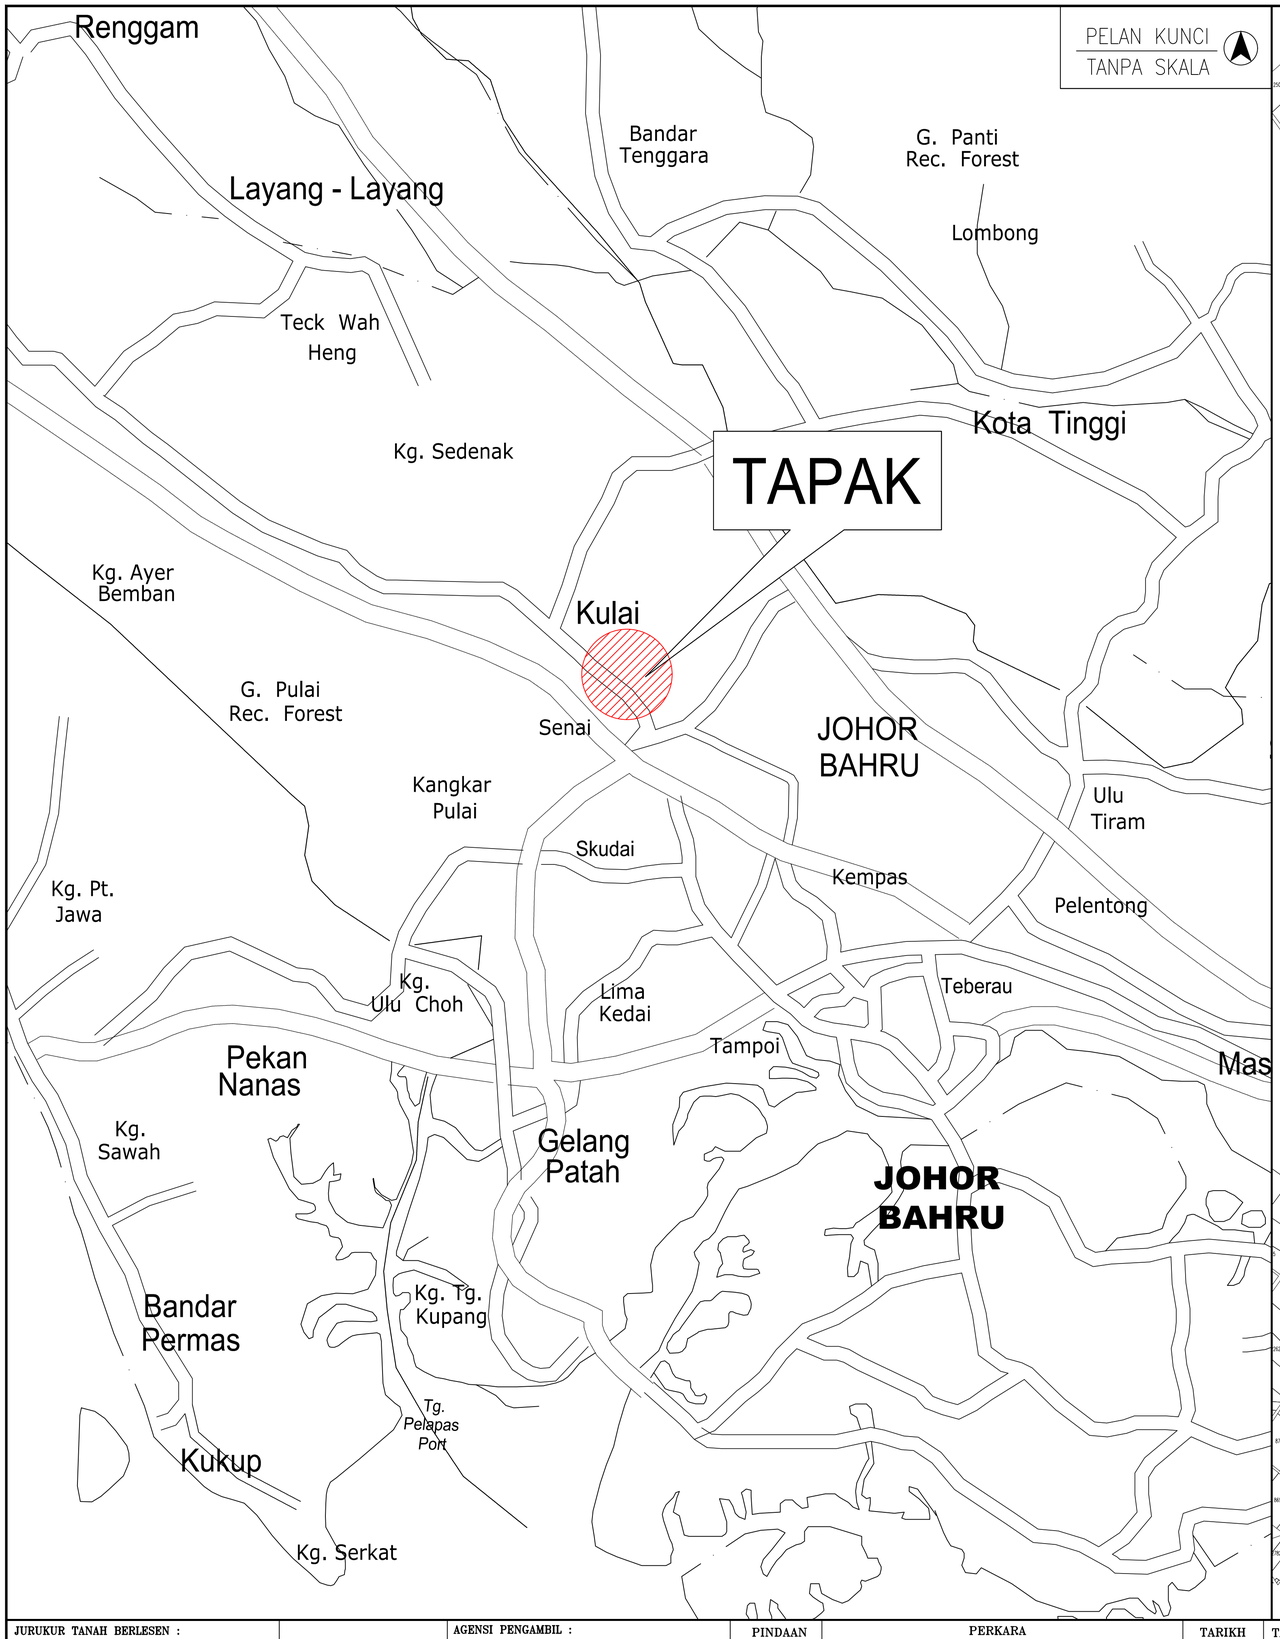

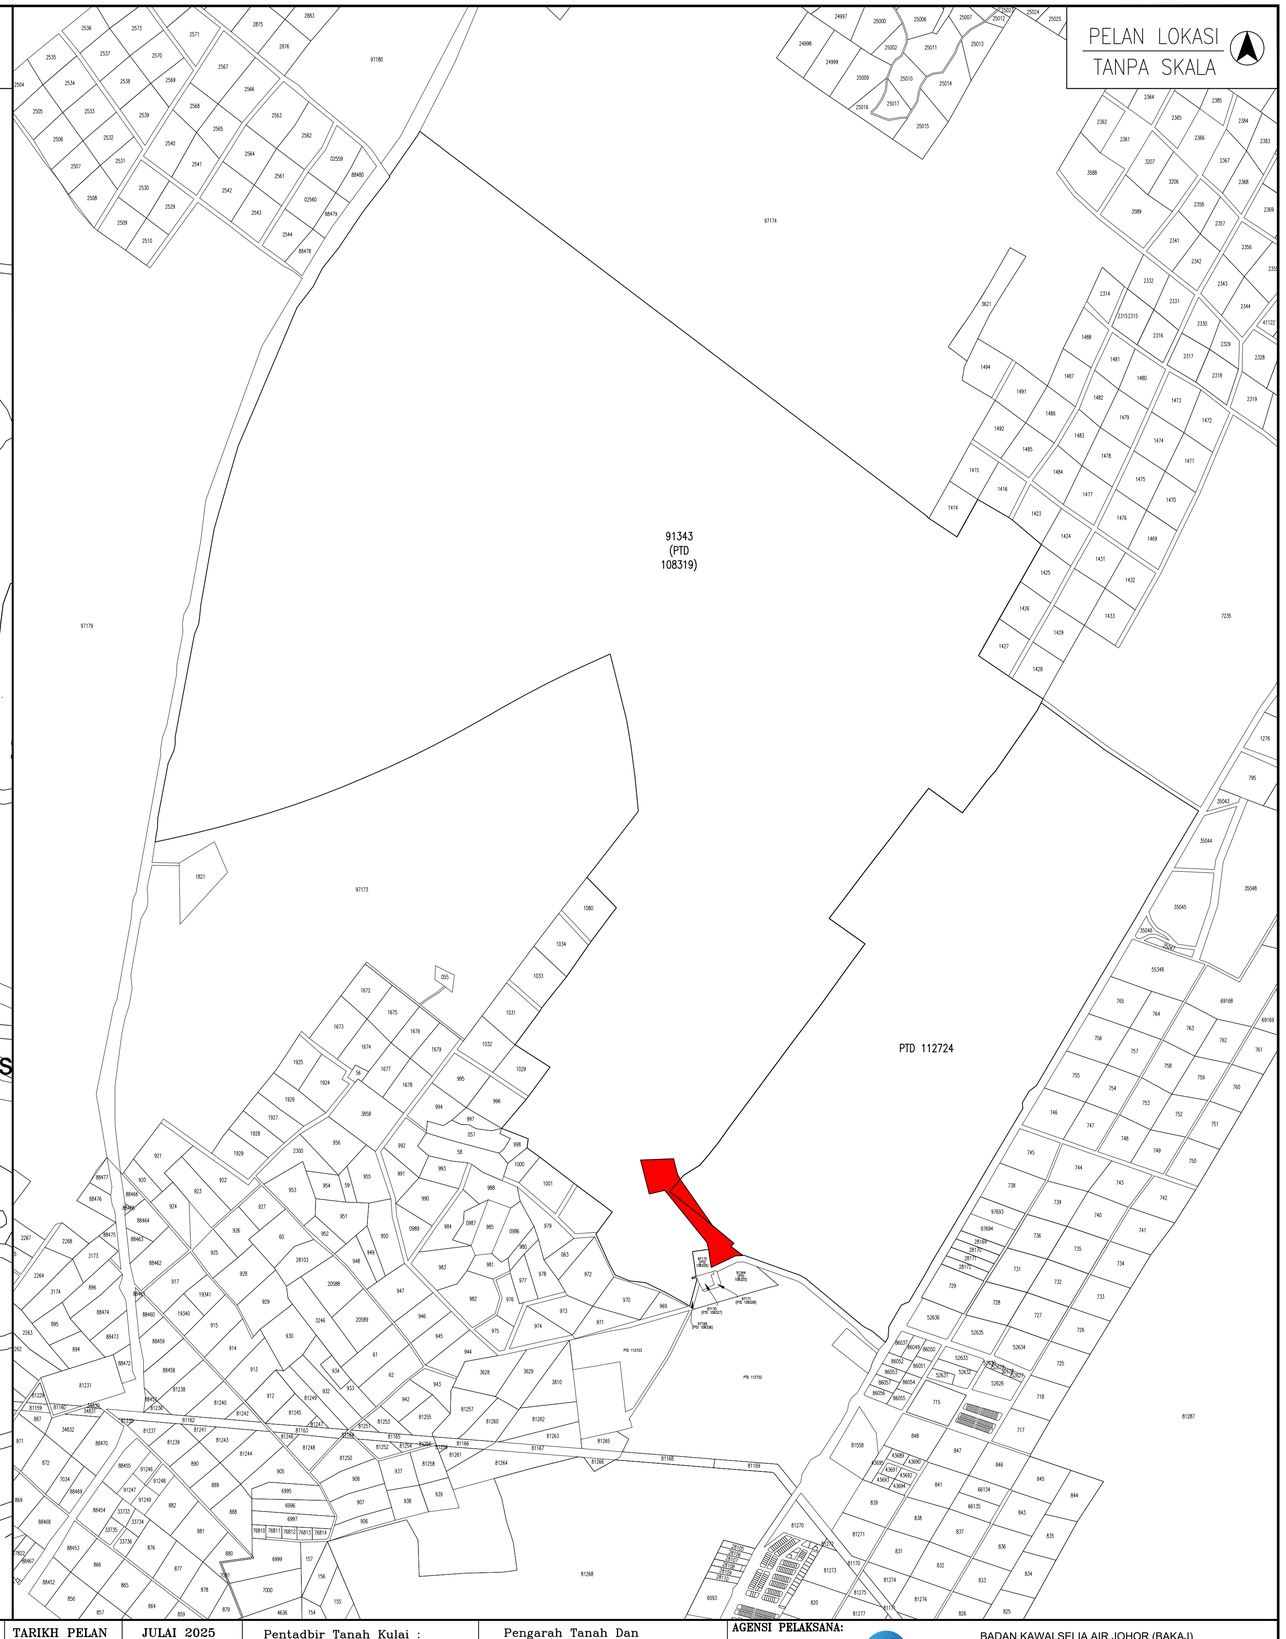

JURUKUR TANAH BERLESEN :

JURUKUR ABADI

Topographical, Cadastral, Engineering Survey Services
Land Development Consultant
No.6-1, Jalan Padi Emas 4/5
Pusat Bandar Tampoi
81200 Johor Bahru
Tel 07-2387244 Fax 07-2380235
E-mail: jurukur_abadi@yahoo.com

LS:HJ.AHMAD RUSTAM BIN HJ. RAMLEY
Licensed Land Surveyor
M.A.A.L.S. PKT (N)
JURUKUR TANAH YANG DILESEN
Dibawah Akta 458 (Disemak 1991)

AGENSI PENGAMBIL :

Ranhill SAJ

PINDAAN	PERKARA	TARIKH

TARIKH PELAN	JULAI 2025
TANPA SKALA	
Diukur oleh	: ADI
Dilukis oleh	: IMA
Disemak oleh	: AKMAL

Pentadbir Tanah Kulai :

Pengarah Tanah Dan Galian Johor :

AGENSI PELAKSANA:

BAKAJ

BADAN KAWALSELIA AIR JOHOR (BAKAJ)
Aras 4, Bangunan Dato' Mohamad Ibrahim Munsyi,
Kota Iskandar
79503 Iskandar Puteri,
Johor Darul Ta'zim.

TAJUK : CADANGAN PEMBANGUNAN INFRASTRUKTUR BEKALAN AIR BAGI WILAYAH PEMBANGUNAN ISKANDAR, NEGERI JOHOR

TAJUK PELAN : PELAN PERMOHONAN PENGAMBILAN BALIK TANAH SEKSYEN 8 DI BAWAH 3(1)(b), AKTA PENGAMBILAN TANAH 1960, DI ATAS LOT 91343 DAN PTD 112724, BAGI KERJA MEMBINA DAN MENYIAPKAN KOLAM AIR BUKIT KULAI BERKAPASITI 18.2 JUTA LITER.

NO LUKISAN : JA(J)01_2025 RANHILL BUKIT KULAI/LA/PELAN INDEKS

NO SYIT :

MUKIM SENAI
DAERAH KULAI
NEGERI JOHOR

SYIT PIAWAI 59 A I, II, III
& 58 D II
SKALA 1:12,500

Line Table		
Line #	Direction	Length
1	223°13'40"	20.173
2	127°19'20"	69.487
4	267°13'40"	34.493
5	244°23'40"	125.276
6	352°02'40"	84.927
7	262°02'20"	75.997
8	172°02'30"	116.433
9	253°54'00"	19.999
10	163°54'00"	6.000
11	73°53'50"	20.000
12	153°24'30"	7.570
13	195°17'30"	131.182
3	87°11'20"	6.447

PEMBESARAN
SKALA 1:3000

PLOT 1
50517.888 mp
5.0518 ha
12.4832 ek

PLOT 2
9359.364 mp
0.9359 ha
2.3127 ek

PTD 112724
3099694.000 mp
309.9694 ha
765.951 ek

91343
(PTD 108319)
9999434.194 mp
999.943 ha
2470.914 ek

KAD 2
129.154 EK

KAD 6
101.183 EK

KAD 5
88.976 EK

KAD 3
113.745 EK

KAD 4
99.576 EK

LIHAT PEMBESARAN

KAD 3 BERTINDIH PLOT 2 (SEK. 8)
= 9.304 mp / 0.930 ha / 2.299 ek

KAWASAN HIJAU KAD 2 - KAD 6 (DITINDIH)
Sumber: snapshot Pelan Rujukan SBKS, dijajarkan pada PTD 112724
BERTINDIH DGN PLOT 2 PENGAMBILAN SEK. 8
Sisihan garis luar vs sempadan PTD: purata 2.1 m (p95 6.8 m).
Anggaran sahaja - bukan hasil ukuran. Lihat muka surat 4.

PETUNJUK :

- LOT TERLIBAT
- TANAH BERMILIK YANG AKAN DIAMBIL
- SIMPANAN JALAN
- TANAH KERAJAAN YANG AKAN DIAMBIL

SENARAI LOT YANG TERLIBAT DENGAN PENGAMBILAN TANAH (TANAH PERSENDIRIAN)

BIL	DAERAH	MUKIM	NO.LOT	HAKMILIK	No.P.AKUI	SYIT PIAWAI	KELUASAN ASAL LOT			KELUASAN YANG DIAMBIL			BAKI LUAS			JENIS KEGUNAAN TANAH	CATITAN
							mp	Hektar	Ekar	mp	Hektar	Ekar	mp	Hektar	Ekar		
1	KULAI	SENAI	91343	GRN 633942	PA 241424	59 A I, II & III	9,999,000.000	999.9000	2,470.807	50,517.888	5.0518	12.483	9,948,482.112	994.8482	2,458.323	KELAPA SAWIT	
2	KULAI	SENAI	PTD 112724	HSD 74877	-	58 D II	3,099,694.000	309.9694	765.951	9,359.364	0.9359	2.313	3,090,334.636	309.0335	763.638	KELAPA SAWIT	

JURUKUR TANAH BERLESEN :

JURUKUR ABADI
Topographical, Cadastral, Engineering Survey Services
Land Development Consultant
No.6-1, Jalan Padi Emas 4/5
Pusat Bandar Tampoi
81200 Johor Bahru
Tel 07-2387244 Fax 07-2380235
E-mail: jurukur_abadi@yahoo.com

LS:HJAHMAD RUSTAM BIN HJ RAMLEY
Licensed Land Surveyor
M.A.A.L.S. 1985 (M)
JURUKUR TANAH YANG DILESEN
Dibawah Akta 458 (Disemak 1991)

AGENSI PENGAMBIL :

Ranhill SAJ

PINDAAN	PERKARA	TARIKH

TARIKH PELAN : JULAI 2025

SKALA
1 : 12,500

Diukur oleh : ADI
Dilukis oleh : IMA
Disemak oleh : AKMAL

Pentadbir Tanah Kulai :

Pengarah Tanah Dan Galian Johor :

AGENSI PELAKSANA:

BAKAJ
BADAN KAWALSELIA AIR JOHOR (BAKAJ)
Aras 4, Bangunan Dato' Mohamad Ibrahim Munsyi,
Kota Iskandar
79503 Iskandar Puteri,
Johor Darul Ta'zim.

TAJUK : CADANGAN PEMBANGUNAN INFRASTRUKTUR BEKALAN AIR BAGI WILAYAH PEMBANGUNAN ISKANDAR, NEGERI JOHOR


TAJUK PELAN : PELAN PERMOHONAN PENGAMBILAN BALIK TANAH SEKSYEN 8 DI BAWAH 3(1)(b), AKTA PENGAMBILAN TANAH 1960, DI ATAS LOT 91343 DAN PTD 112724, BAGI KERJA MEMBINA DAN MENYIAPKAN KOLAM AIR BUKIT KULAI BERKAPASITI 18.2 JUTA LITER.


NO LUKISAN : JA(J)01_2025 RANHILL BUKIT KULAI/LA/SEKSYEN 8

NO SYIT :

KESAN PENGAMBILAN TANAH SEKSYEN 8 (PLOT 2) KE ATAS KAD 3 - PTD 112724

Kolam Air Bukit Kulai 18.2 Juta Liter, Mukim Senai, Daerah Kulai. Pelan asas: JA(J)01_2025 RANHILL BUKIT KULAI/LA/SEKSYEN 8 REV.1 (m/s 3, skala 1:12,500).

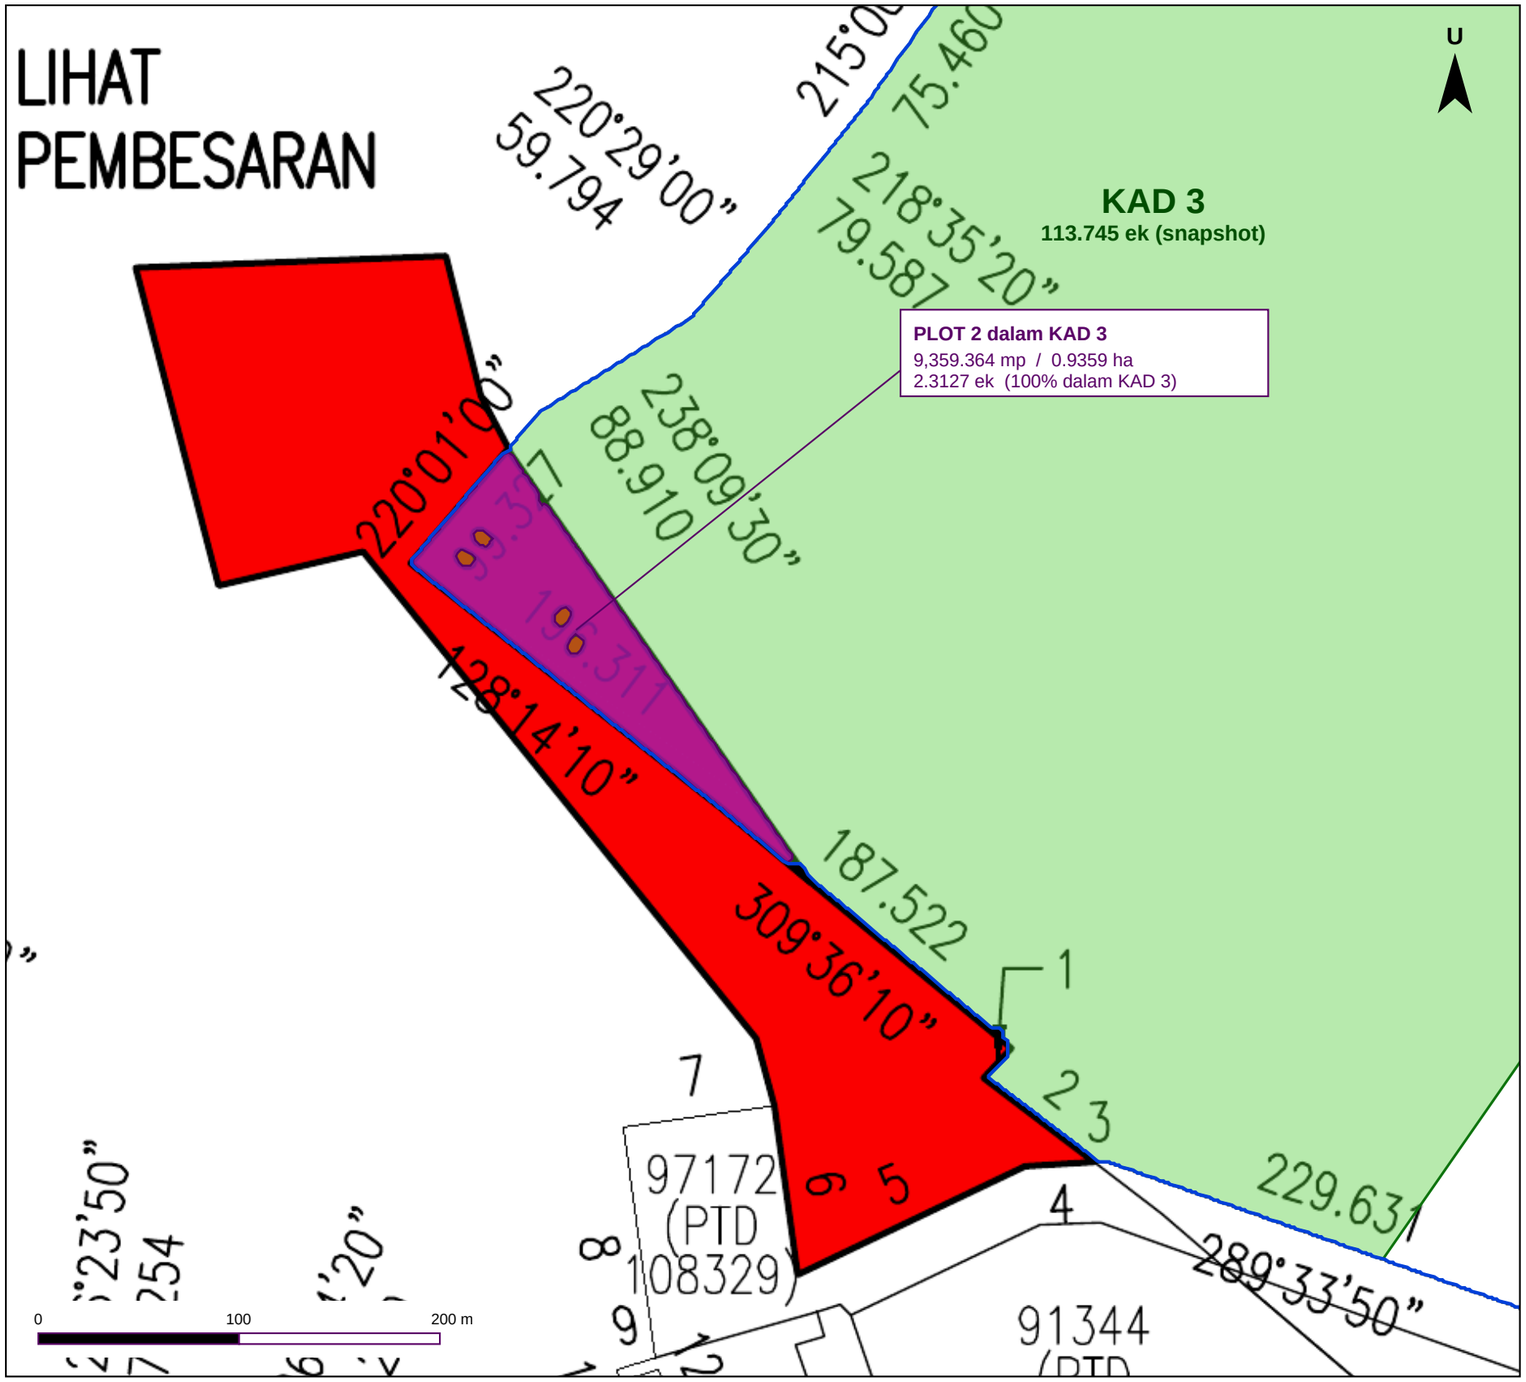

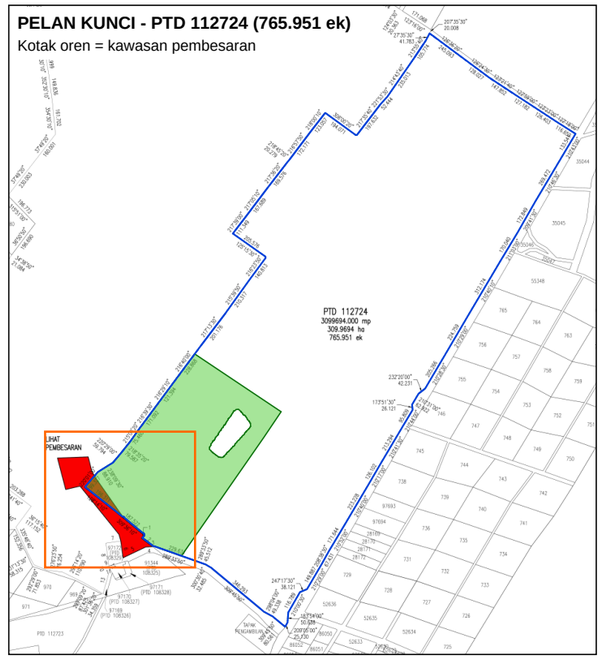

PETUNJUK

- KAD 3 (113.745 ek, ikut snapshot)
- Plot 2 - tanah diambil dalam KAD 3
- Tanah diambil Sek. 8 (Plot 1 dalam lot 91343)
- Sempadan PTD 112724

KELUASAN

	mp	Hektar	Ekar
KAD 3 (snapshot)	460,309.681	46.0310	113.7450
Plot 2 diambil (dalam KAD 3)	9,359.364	0.9359	2.3127
BAKI KAD 3	**450,950.317**	**45.0950**	**111.4323**

Peratus KAD 3 terjejas: 2.03%

KAD 2, 4, 5 dan 6: tidak terjejas.

KAEDAH

- Plot 2 & sempadan PTD dari vektor pelan PDF Sek. 8 (keluasan disemak: Plot 2 9,351 mp vs jadual 9,359.364 mp; PTD dikalibrasi ke 3,099,694 mp).
- Garis luar planner padan sempadan PTD (sisihan purata ~3 m di penjuru); hujung KAD 3 ikut sudut asal PTD, jadi Plot 2 termasuk dalam KAD 3.
- Sempadan dalaman KAD 3 (dari snapshot) dianjak 11.1 m ke dalam supaya keluasan = 113.745 ek; petak putih dalam KAD 3 dikecualikan.
- Plot 2 terletak >= 355 m dari sempadan dalaman, jadi pelarasan ini tidak mengubah keputusan pertindihan.
- Keluasan Plot 2 & baki ikut jadual pelan Sek. 8; KAD 3 ikut snapshot. Kedudukan KAD 3 anggaran - bukan hasil ukuran.