

KESAN PENGAMBILAN TANAH SEKSYEN 8 (PLOT 2) KE ATAS KAD 3 - PTD 112724

Kolam Air Bukit Kulai 18.2 Juta Liter, Mukim Senai, Daerah Kulai. Pelan asas: JA(J)01_2025 RANHILL BUKIT KULAI/LA/SEKSYEN 8 REV.1 (m/s 3, skala 1:12,500).

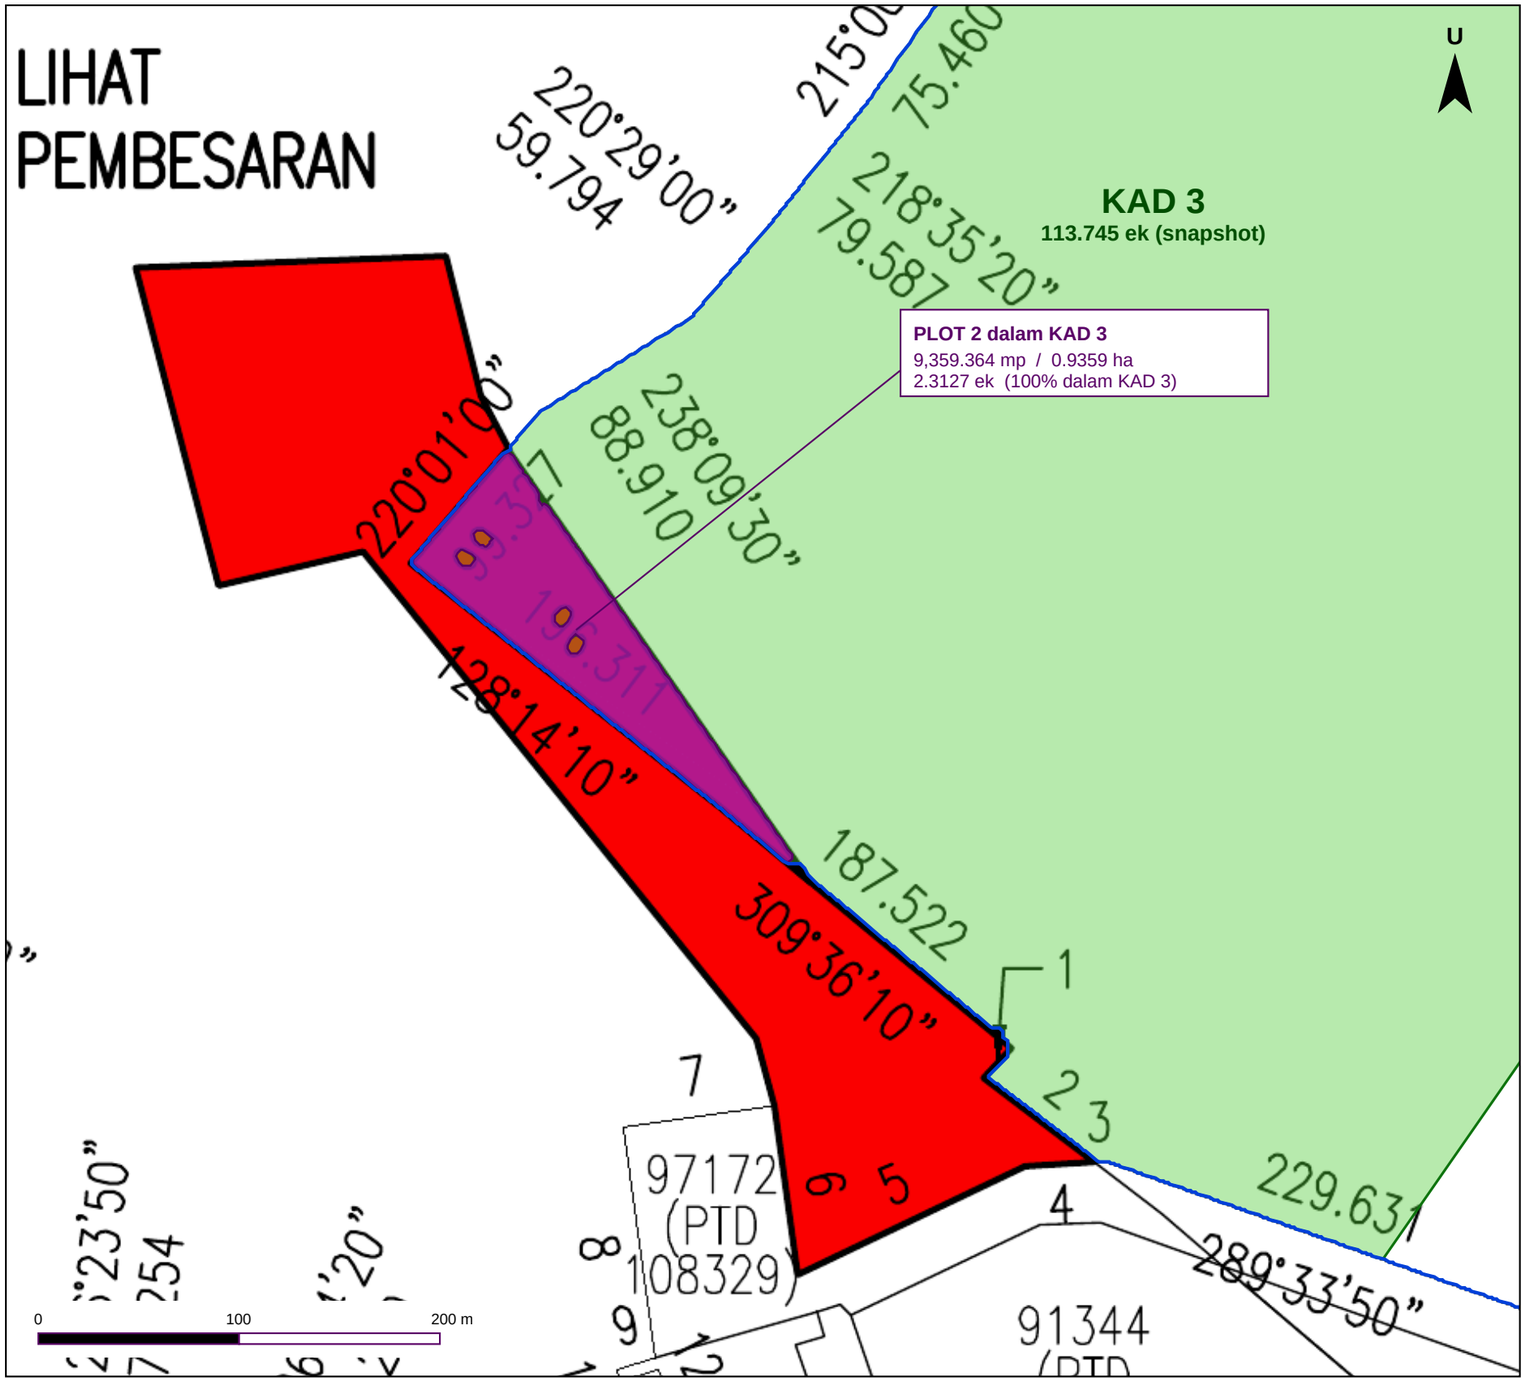

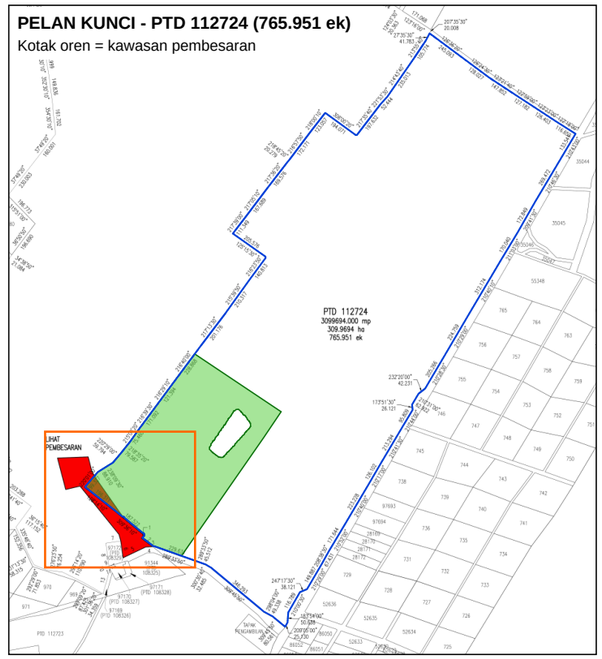

PETUNJUK

- KAD 3 (113.745 ek, ikut snapshot)
- Plot 2 - tanah diambil dalam KAD 3
- Tanah diambil Sek. 8 (Plot 1 dalam lot 91343)
- Sempadan PTD 112724

KELUASAN

	mp	Hektar	Ekar
KAD 3 (snapshot)	460,309.681	46.0310	113.7450
Plot 2 diambil (dalam KAD 3)	9,359.364	0.9359	2.3127
BAKI KAD 3	**450,950.317**	**45.0950**	**111.4323**

Peratus KAD 3 terjejas: 2.03%

KAD 2, 4, 5 dan 6: tidak terjejas.

KAEDAH

- Plot 2 & sempadan PTD dari vektor pelan PDF Sek. 8 (keluasan disemak: Plot 2 9,351 mp vs jadual 9,359.364 mp; PTD dikalibrasi ke 3,099,694 mp).
- Garis luar planner padan sempadan PTD (sisihan purata ~3 m di penjuru); hujung KAD 3 ikut sudut asal PTD, jadi Plot 2 termasuk dalam KAD 3.
- Sempadan dalaman KAD 3 (dari snapshot) dianjak 11.1 m ke dalam supaya keluasan = 113.745 ek; petak putih dalam KAD 3 dikecualikan.
- Plot 2 terletak >= 355 m dari sempadan dalaman, jadi pelarasan ini tidak mengubah keputusan pertindihan.
- Keluasan Plot 2 & baki ikut jadual pelan Sek. 8; KAD 3 ikut snapshot. Kedudukan KAD 3 anggaran - bukan hasil ukuran.